Panel de ramificación: TG-1

Ubicación: HALL 9
Tipo de red eléctrica: CORRIENTE ALTERNA

Voltios: MONOFASICO
Fases: 1


Notas:

CKT	CÓDIGO	CIRCUITO	AMPERAJE	TIPO DE CABLE	AISLAMIENTO	TAMAÑO DE TUBO	VOLTAJE	Carga
1	C-1	ALUMBRADO	15 A	CABLE 2.5 mm2 (N°14)	TW	Ø 20mm PVC-SAP	220 V	104 VA
2	C-2	ALUMBRADO	15 A	CABLE 2.5 mm2 (N°14)	TW	Ø 20mm PVC-SAP	220 V	208 VA
3	C-3	TOMACORRIENTE	20 A	CABLE 4 mm2 (N° 12)	TW	Ø 20mm PVC-SAP	220 V	1600 VA
4	C-4	LAVADORA	20 A	CABLE 4 mm2 (N° 12)	TW	Ø 20mm PVC-SAP	220 V	1200 VA
5	C-5	CALENTADOR 1ER NIVEL	20 A	CABLE 4 mm2 (N° 12)	TW	Ø 20mm PVC-SAP	220 V	1000 VA
6	C-6	COCINA ELÉCTICA	30 A	CABLE 6 mm2 (N° 10)	TW	Ø 20mm PVC-SAP	220 V	6000 VA
7	C-7	TELEFONO PORTERO	15 A	CABLE 2.5 mm2 (N°14)	TW	Ø 20mm PVC-SAP	220 V	200 VA
8	C-8	ELECTROBOMBA	20 A	CABLE 4 mm2 (N° 12)	TW	Ø 20mm PVC-SAP	220 V	1200 VA
9	C-9	ALUMBRADO JARDIN INT.	15 A	CABLE 2.5 mm2 (N°14)	TW	Ø 20mm PVC-SAP	220 V	13 VA
10	C-10	ALUMBRADO	15 A	CABLE 2.5 mm2 (N°14)	TW	Ø 20mm PVC-SAP	220 V	103 VA
11	C-11	TOMACORRIENTE	20 A	CABLE 4 mm2 (N° 12)	TW	Ø 20mm PVC-SAP	220 V	2280 VA
12	C-12	CALENTADOR 2DO NIVEL	20 A	CABLE 4 mm2 (N° 12)	TW	Ø 20mm PVC-SAP	220 V	1000 VA
13								
				Carga total:				**5197 VA**
				Total de amperios:				**47 A**

Clasificación de carga	Carga conectada	Factor de demanda	Demanda estimada
LAVADORA	1200 VA	80.00%	960 VA
CALENTADOR 1ER N.	1000 VA	100.00%	1000 VA
TELEFONO	200 VA	100.00%	200 VA
COCINA ELEC.	6000 VA	80.00%	4800 VA
ELECTROBOMBA	1200 VA	50.00%	600 VA
CALENTADOR 2DO N.	1000 VA	100.00%	1000 VA
ALUMBRADO & TOMACORRIENTE	4307 VA	65.19%	2807 VA


Totales de panel	
Carga total conectada:	14907 VA
Total de demanda estimada:	11367 VA
Corriente total conectada:	68 A
Demanda de corriente total...	52 A

Notas:

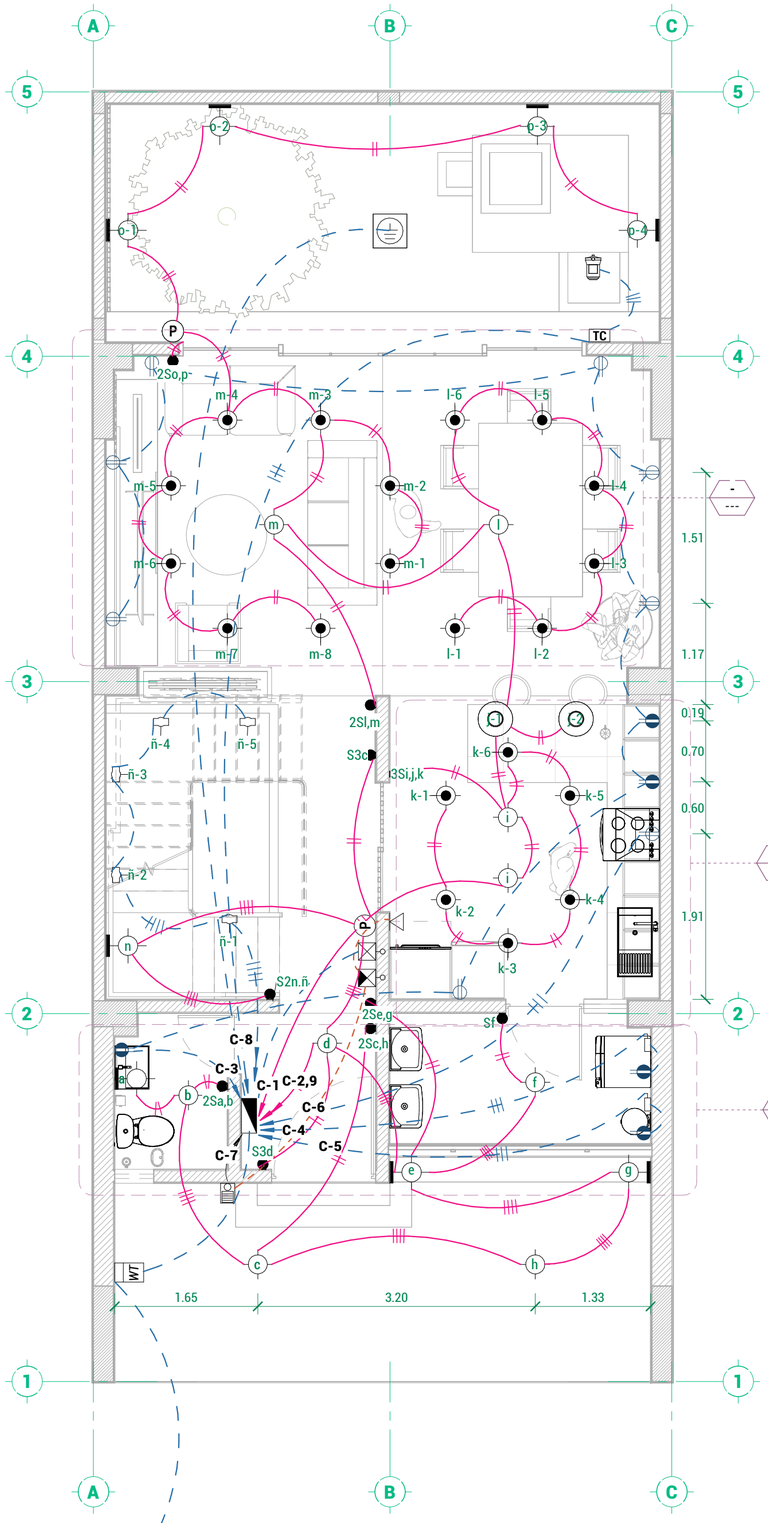


1 Plano de planta electricas

1 : 50

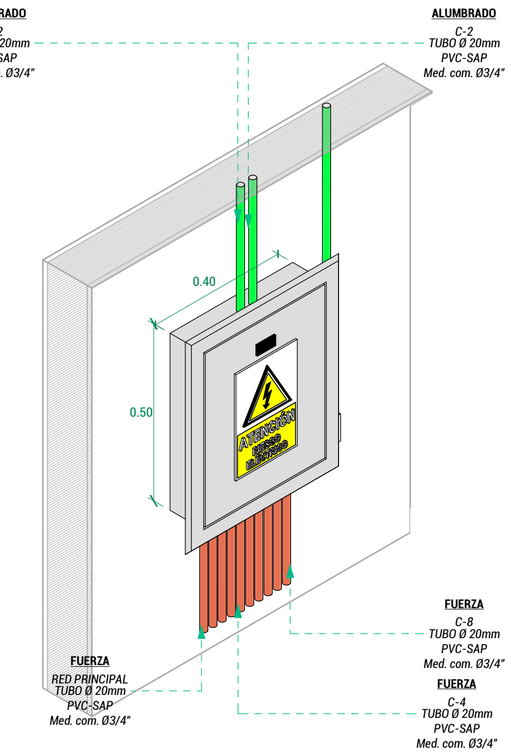

2 TABLERO ELECTRICO

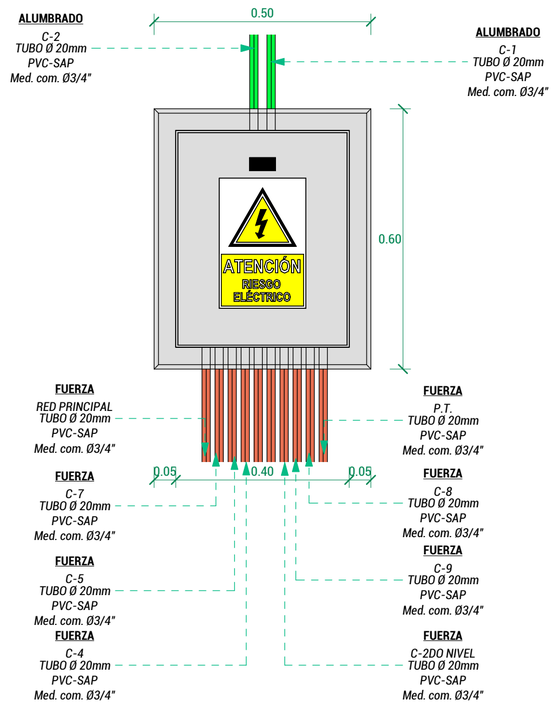

3 TABLERO ELECTRICO

1 : 10

0 1 2 3 4 5 10 m

ANKA STUDIO

Proyecto:
VIVIENDA UNIFAMILIAR

Número de Proyecto: 0001
Estado del Proyecto:
Ubicación del Proyecto:

Puno - Perú

Nombre de Plano:
PLANTA IE PRIMER NIVEL

Cliente:	**ANKA Studio**
Dibujado por:	**ARQ. Yhovel Alex Merma Ari**
Revisado por:	**ING. Angel Yana**
Fecha:	**12/01/2025 7:57:47**
Escala:	**Como se indica**

Lámina No.
IE101