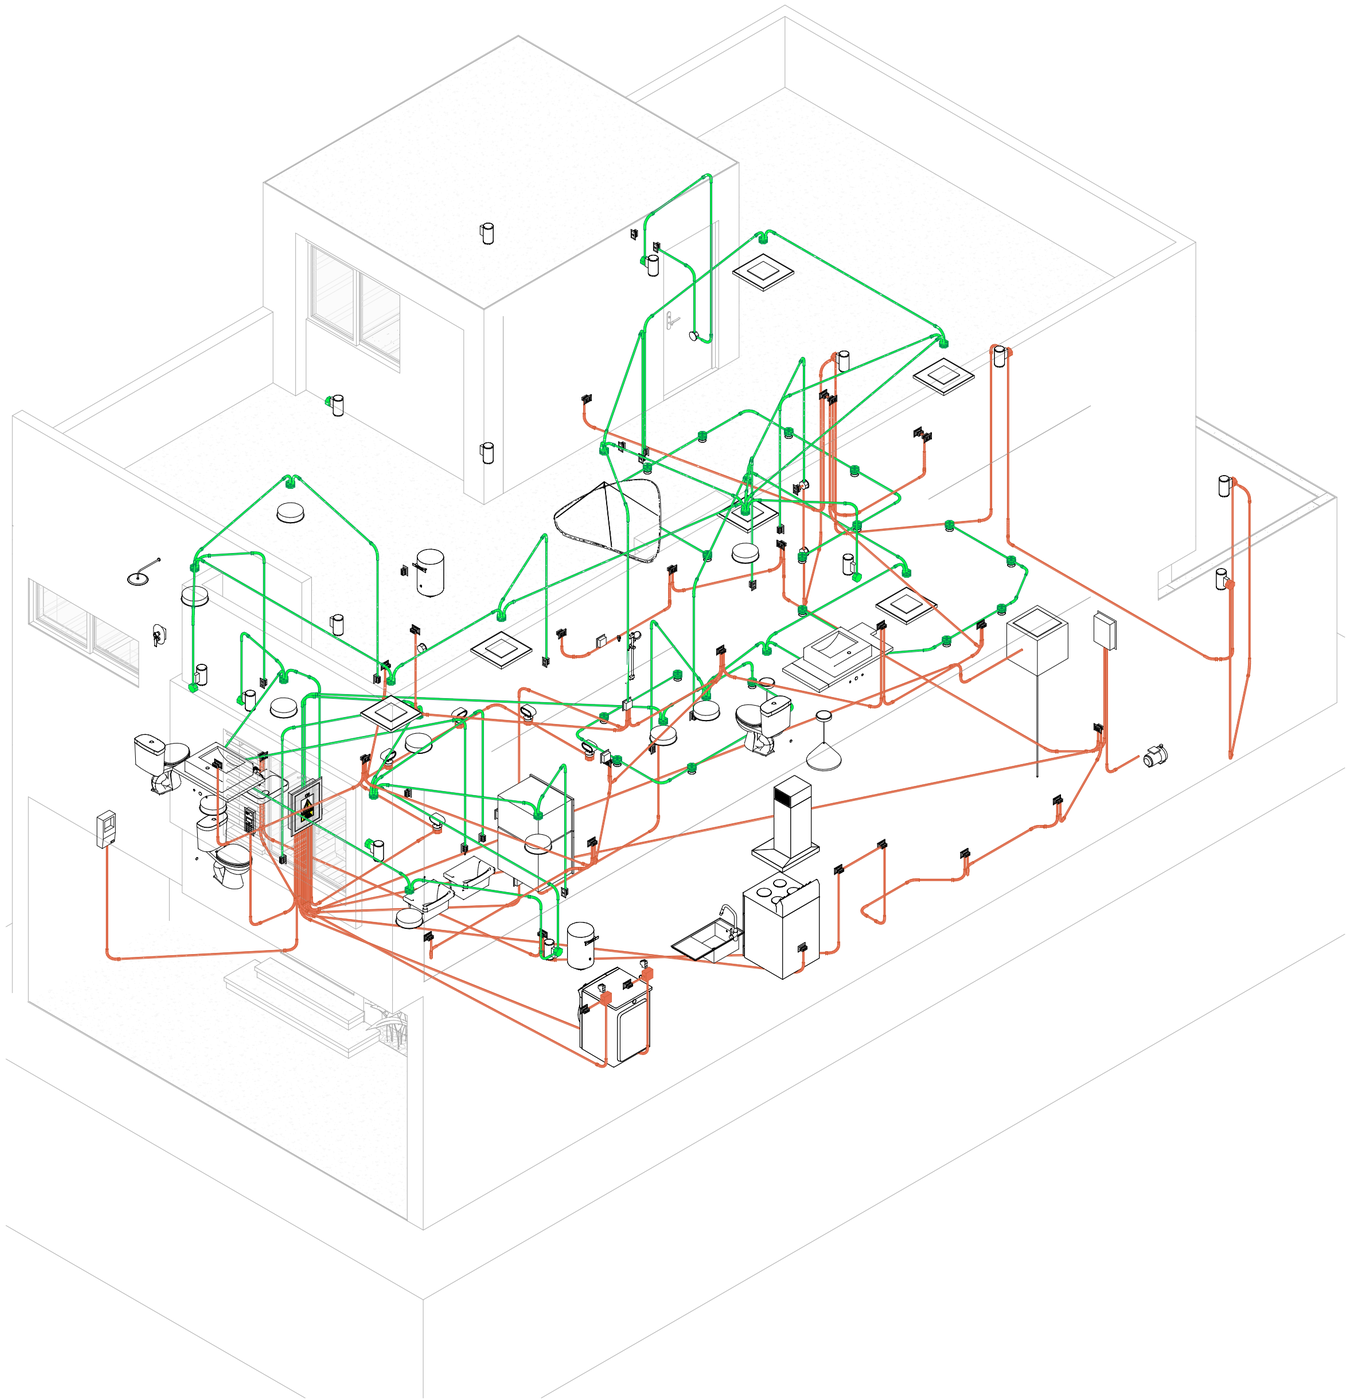


LEYENDA

SIMBOLO	DESCRIPCION	ALTURA m	TIPO DE CAJA (mm)
	SALIDA PARA ALUMBRADO DE TECHO	----	OCT-100x40
	SALIDA PARA BRAQUETE EN LA PARED	2.00	OCT-100x40
	INTERRUPTOR DE 1, 2 Y 3 TIEMPOS	1.20	RECT. 100x55x50mm
	NTERRUPTOR DE COMMUTACION DE 3 VIAS	1.20	RECT. 100x55x50mm
	INTERRUPTOR DE PALANCA CON FUSIBLE DE PROTECCION	1.20	ESPECIAL
	TOMACORR. DOBLE TIPO UNIVERSAL CON TOMA A TIERRA A PRUEBA DE AGUA	0.30/1.10	RECT. 100x55x50
	CAJA DE PASO CON TAPA CIEGA	0.30/2.10	OCT-100x40
	CAJA DE PASO CUADRADA DE 100x40mm SALVO INDICACION	0.30	CUAD-100x40
	TABLERO DE DISTRIBUCION ELECTRICA	1.80 Borde Sup	ESPECIAL
	INTERRUPTOR AUTOMATICO TERMOMAGNETICO	----	----
WH	MEDIDOR KW-H	ESPECIAL	ESPECIAL
	POZO DE TOMA A TIERRA	----	----
	TUBERIA EMPOTRADO EN TECHO O PARED 2-1x25mm2 TW-20MM∅ PVC, SALVO INDICACION	----	----
	TUBERIA EMPOTRADO EN PISO 2-1x4mm2 TW + 1x4 mm2/T -20MM∅ PVC-P, SALVO INDICACION	----	----
	SALIDA DE FUERZA MONOFASICO CON TOMA A TIERRA	0.40	CUAD-100x40
	TOMACORRIENTE DOBLE TIPO UNIVERSAL	0.30	RECT. 100x55x50
TC	TABLERO DE CONTROL (SUMINISTRADO POR PROVEEDOR DE EQUIPO)	1.80 Bde.Sup.	ESPECIAL
	TUBERIA PARA SIST. DE TELEFONO EXT. 20mm∅ PVC-P s/a EMPOTRADA EN PISO O PARED	----	----
	SALIDA PARA TELEFONO EXTERNO EN LA PARED	0.30	CUAD-100x40
	TUBERIA PARA SISTEMA DE INTERCOMUNICADORES 20mm∅ PVC-P EMPOTRADA EN PISO O PARED, SALVO INDICACION	----	----
	DIRECTORIO TELEFONO PORTERO O INTERCOMUNICADOR	1.40	ESPECIAL
	SALIDA PARA TELEFONO INTERNO O INTERCOMUNICADOR	1.40	CUAD-100x40
	TUBERIA PARA SISTEMA DE TELECABLE 20mm∅ PVC-P s/a EMPOTRADA EN PISO O PARED, SALVO INDICACION	----	----
TV	SALIDA PARA TELEVISION POR CABLE	0.30/1.80	CUAD-100x40
	SALIDA PARA CALENTADOR ELECTRICO	1.20	RECT. 100x55x50mm
	CAJA DE PASO CUADRADA DE 100x40mm SALVO INDICACION PARA SISTEMA DE TELEFONO EXTERNO	0.40	ESPECIAL
	CAJA DE PASO CUADRADA DE 100x40mm SALVO INDICACION PARA SISTEMA DE TELEFONO INTERNO (INTERCOMUNICADOR)	0.40	ESPECIAL
	CAJA DE PASO CUADRADA DE 100x40mm SALVO INDICACION PARA SISTEMA DE TV - CABLE	0.40	ESPECIAL

1

VISTA 3D
ALUMBRADO-TOMACORRIENTE

0 1 2 3 4 5 10 m

ANKA STUDIO

Proyecto:
VIVIENDA UNIFAMILIAR

Número de Proyecto: 0001

Estado del Proyecto:

Ubicación del Proyecto:

Puno - Perú

Nombre de Plano:
ISOMETRICO

Cliente: **ANKA Studio**

Dibujado por: **ARQ. Yhovel Alex Merma Ari**

Revisado por: **ING. Angel Yana**

Fecha: **12/01/2025 7:58:06**

Escala: **1 : 50**

Lámina No.
IE102