
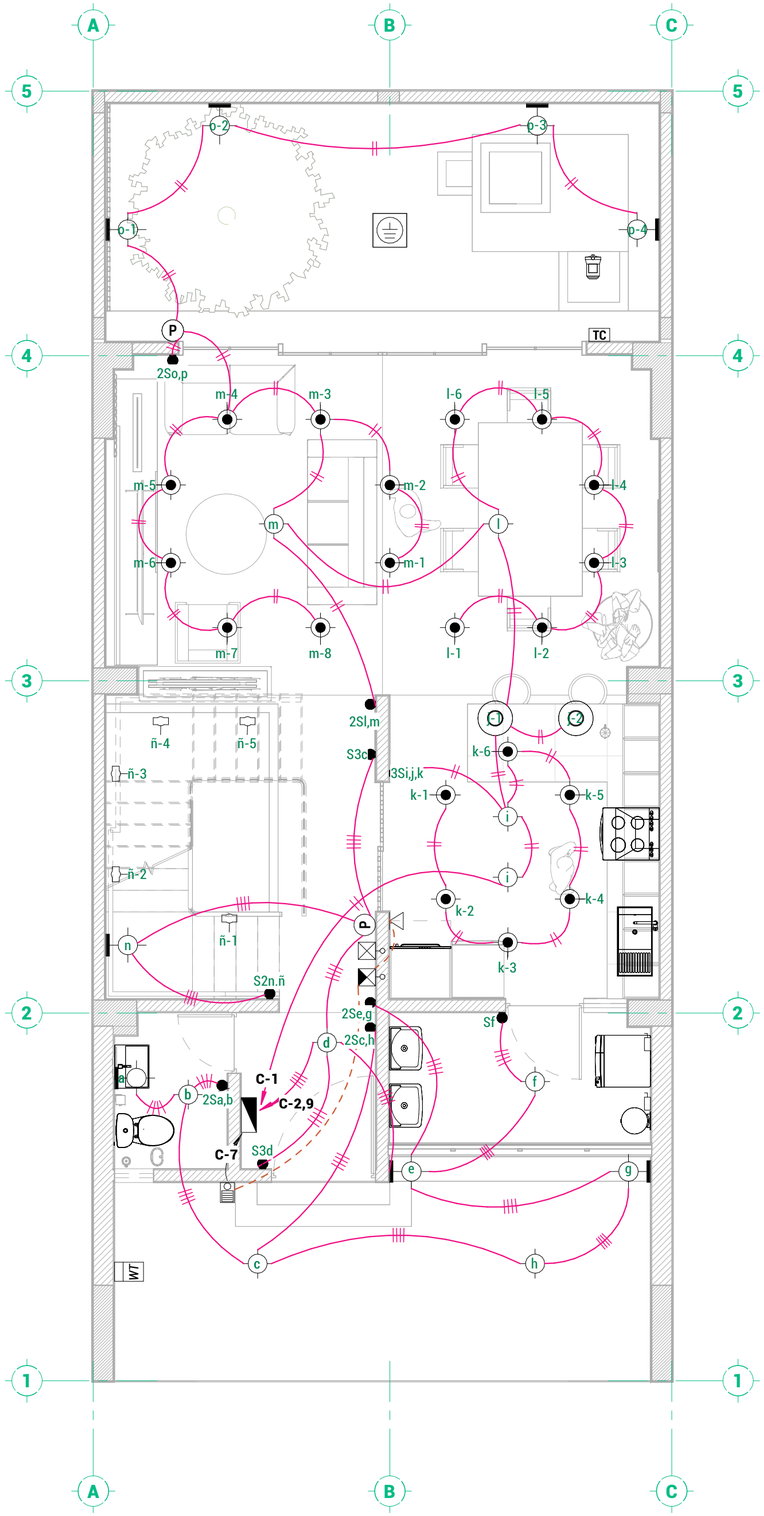


1 PLANTA 1ER NIVEL ALUMBRADO

1 : 50

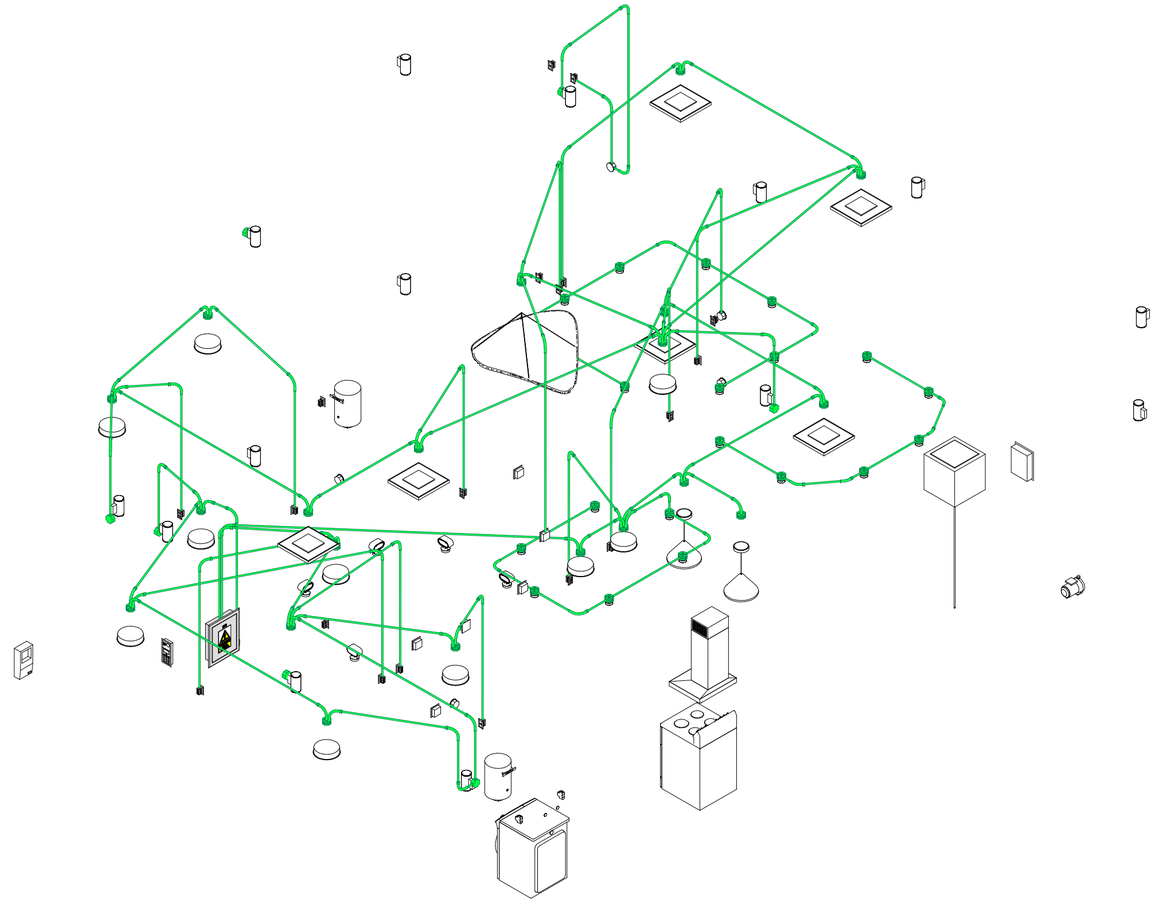

2 VISTA 3D ALUMBRADO

0 1 2 3 4 5 10 m

ANKA STUDIO

Proyecto:

VIVIENDA UNIFAMILIAR

Número de Proyecto:	0001
Estado del Proyecto:	

Ubicación del Proyecto:

Puno - Perú

Nombre de Plano:

PLANTA 1ER NIVEL ALUMBRADO

Cliente:	**ANKA Studio**
Dibujado por:	**ARQ. Yhovel Alex Merma Ari**
Revisado por:	**ING. Angel Yana**
Fecha:	**12/01/2025 7:58:13**
Escala:	**1 : 50**

Lámina No.

IE103