

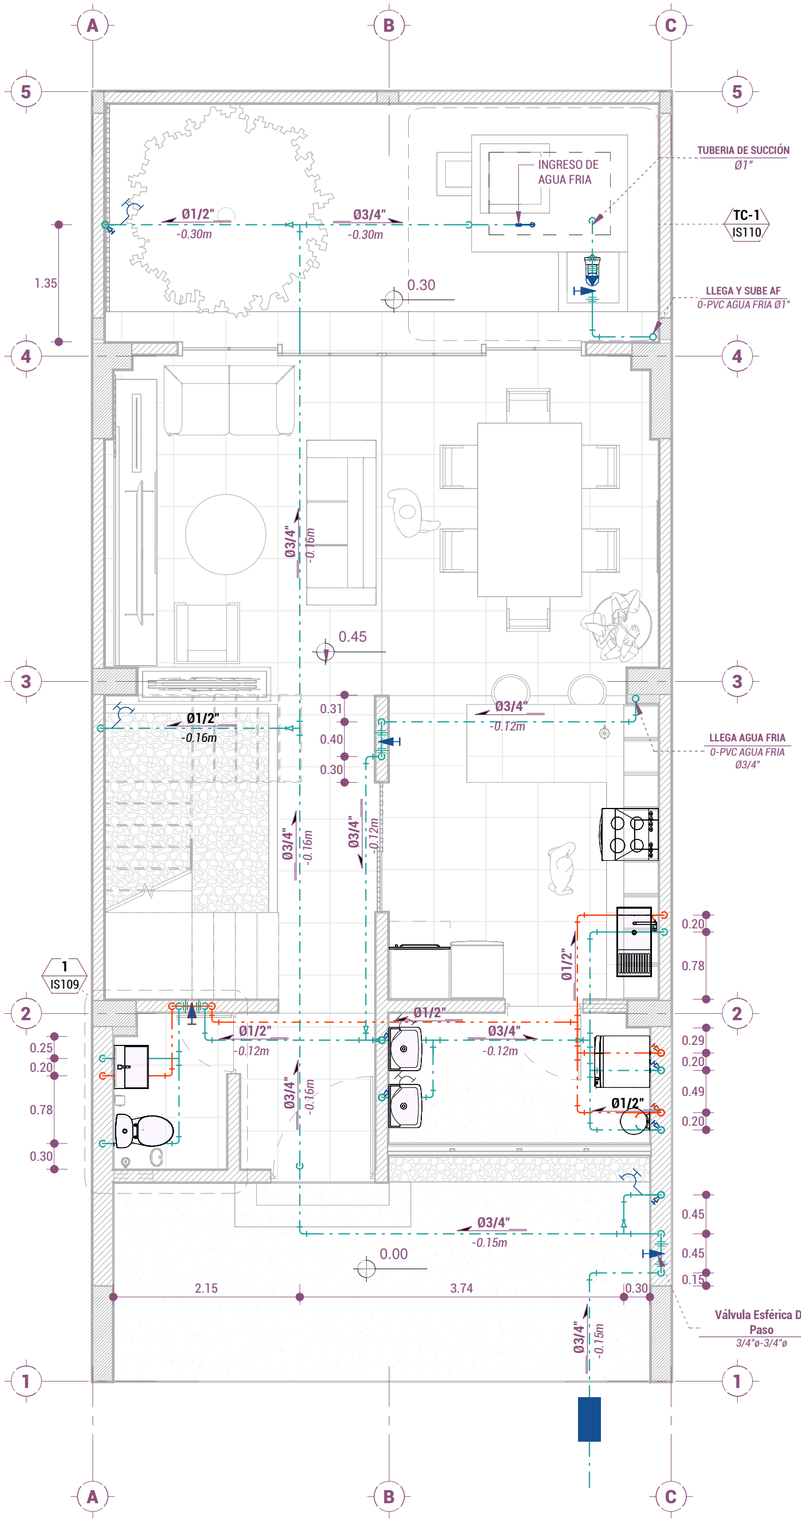


P-1 Planta general AF/AC-1ER NIVEL

1 : 50

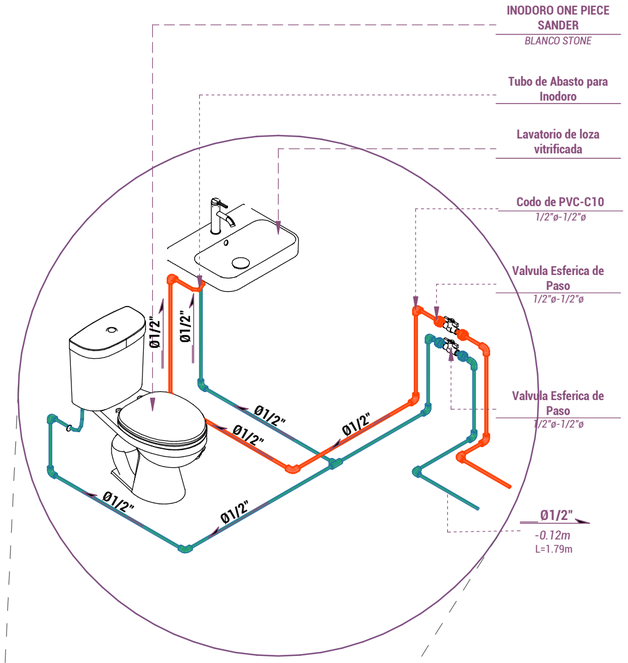

I-1 3D AF/AC 1ER NIVEL DETALLE

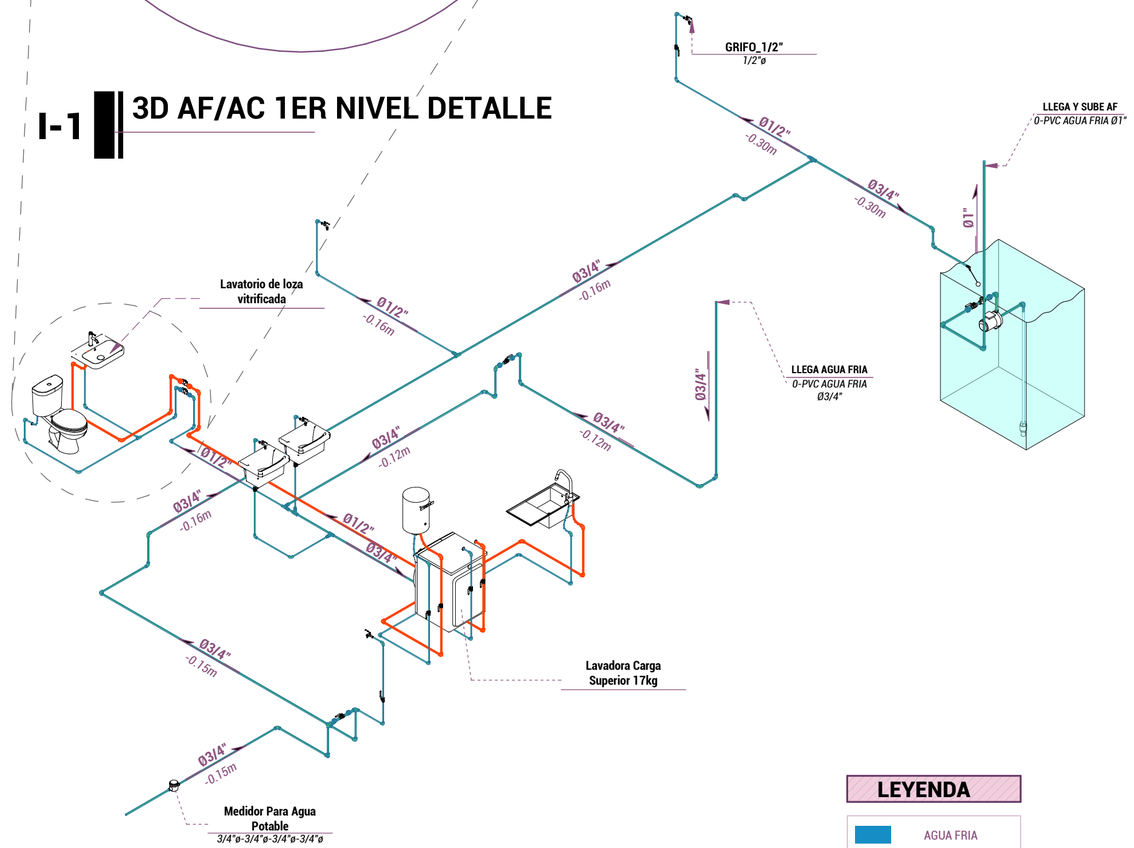

IS-1 3D AF/AC 1ER NIVEL

LEYENDA

INSTALACIONES HIDROSANITARIAS	
SIMBOLO	DESCRIPCION
	Medidor de Agua
	Tubería de Agua Fría
	Tubería de Agua Caliente
	Cruce Sin Conexión
	Codo de 90°
	Tee
	Válvula de Compuerta
	Válvula Check
	Válvula de Riego
	Calentador Eléctrico
	Filtro de Agua
	Electrobomba

LEYENDA

AGUA FRIA

AGUA CALIENTE

0 1 2 3 4 5 10 m

ANKA STUDIO

Proyecto: **VIVIENDA UNIFAMILIAR**

Número de Proyecto: 0001

Estado del Proyecto:

Ubicación del Proyecto:

Puno - Perú

Nombre de Plano: **PLANIMETRIA AF/AC 1ER NIVEL**

Cliente:	ANKA Studio
Dibujado por:	ARQ. Yhovel Alex Merma Ari
Revisado por:	ING. Angel Yana
Fecha:	11/01/2025 18:51:57
Escala:	1 : 50

Lámina No. **IS101**