
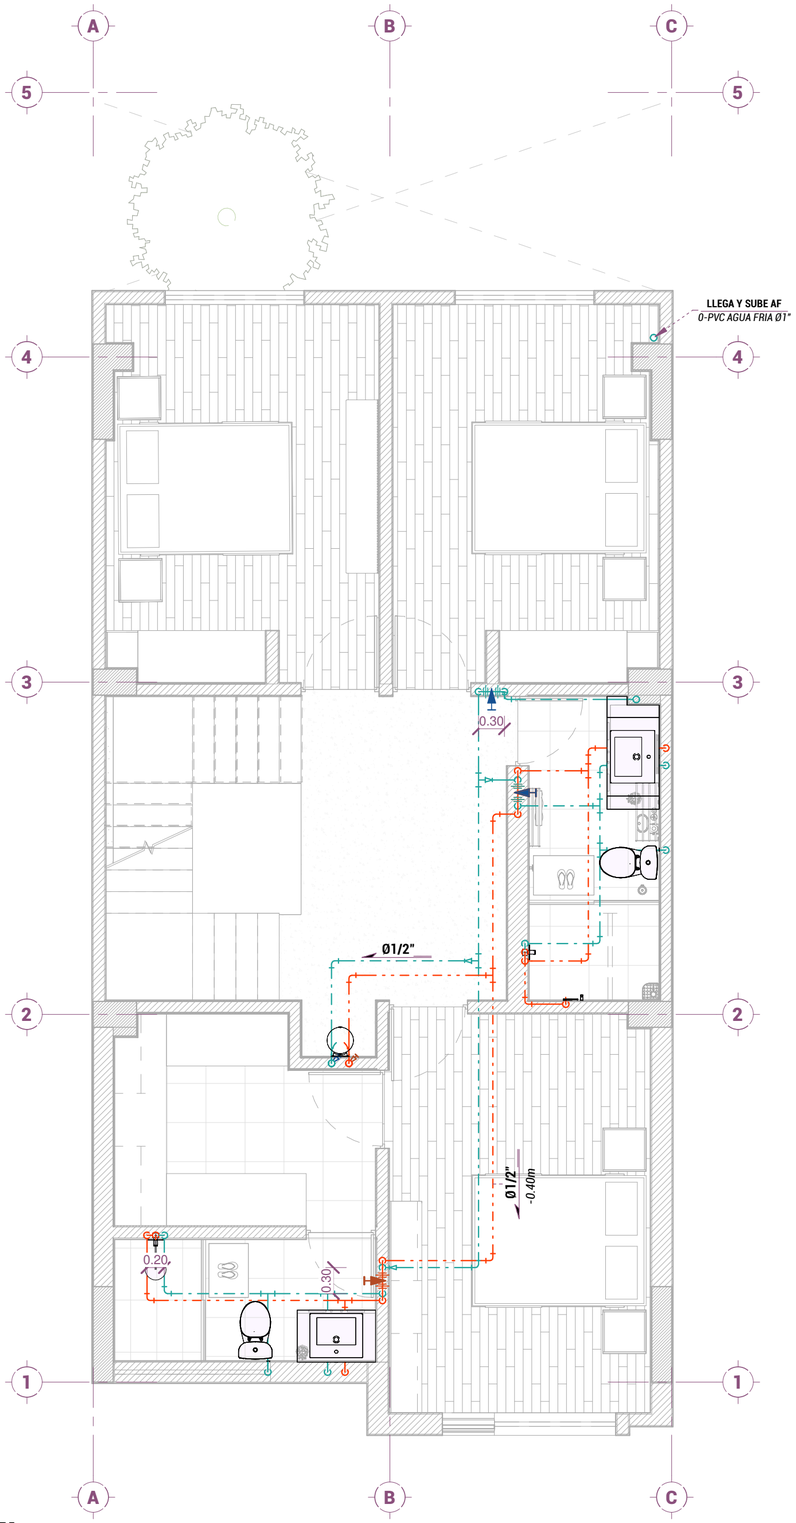


1 Planta general AF/AC-2DO NIVEL


1 : 50

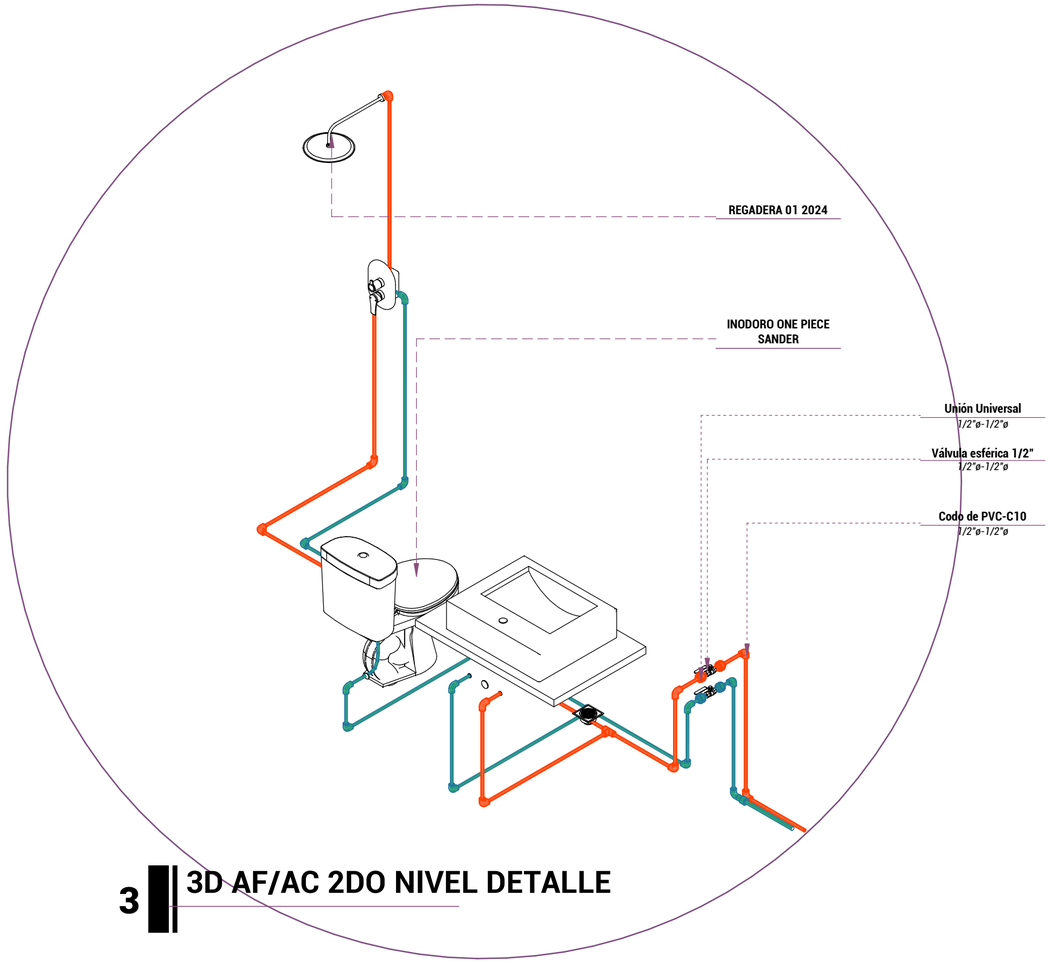

3 3D AF/AC 2DO NIVEL DETALLE

LEYENDA

INSTALACIONES HIDROSANITARIAS	
SIMBOLO	DESCRIPCION
	Medidor de Agua
	Tubería de Agua Fría
	Tubería de Agua Caliente
	Cruce Sin Conexión
	Codo de 90°
	Tee
	Válvula de Compuerta
	Válvula Check
	Válvula de Riego
	Calentador Eléctrico
	Filtro de Agua
	Electrobomba

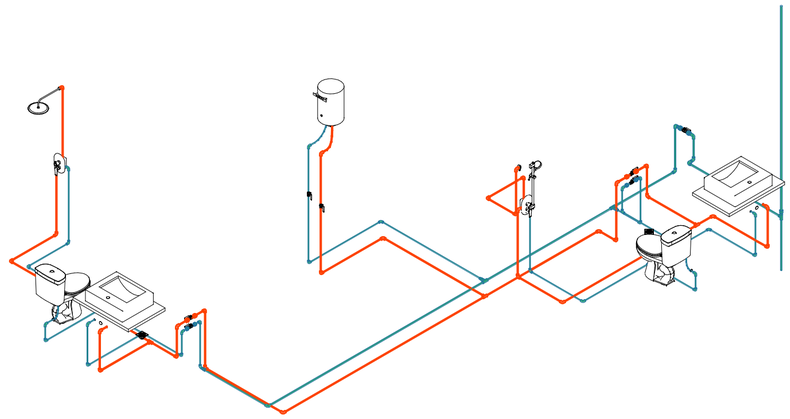

2 3D AF/AC 2DO NIVEL

0 1 2 3 4 5 10 m

ANKA STUDIO

Proyecto:

VIVIENDA UNIFAMILIAR

Número de Proyecto: 0001

Estado del Proyecto:

Ubicación del Proyecto:

Puno - Perú

Nombre de Plano:

PLANIMETRIA AF/AC 2DO NIVEL

Cliente:	**ANKA Studio**
Dibujado por:	**ARQ. Yhovel Alex Merma Ari**
Revisado por:	**ING. Angel Yana**
Fecha:	**12/01/2025 8:25:11**
Escala:	**1 : 50**

Lámina No.

IS102