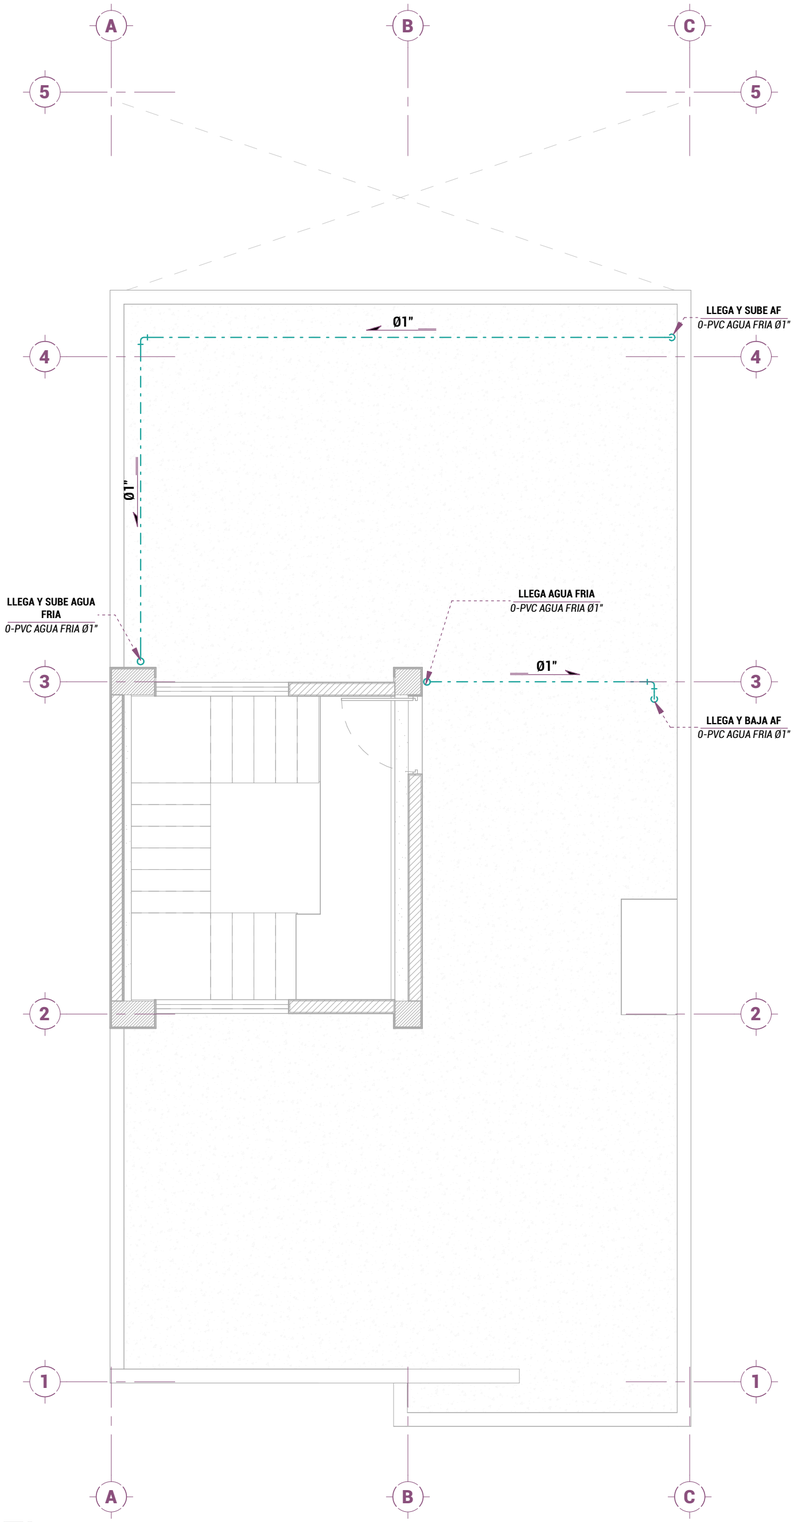



1 Planta general AF/AC-3ER NIVEL

1 : 50

ESPECIFICACIONES TÉCNICAS


RED DE AGUA:

- Todos los materiales, tuberías y accesorios a utilizarse en las redes de agua fría, caliente y desagüe serán de buena calidad, de acuerdo con las normas técnicas de "ITINTEC" y con las disposiciones estipuladas en el Reglamento Nacional de Construcciones del Perú.
- Las tuberías para agua fría serán de PVC rígido, clase 10, de unión a presión simple y/o unión roscada, incluyendo sus accesorios.
- Las tuberías para agua caliente serán de C-PVC rígido de unión a presión simple y/o unión roscada, y accesorios del mismo material.
- Se utilizará pegamento especial para C-PVC, con aislamiento térmico apropiado.
- Las válvulas de compuerta serán de asiento de bronce. En cada válvula se instalará una unión universal cuando se trate de tuberías visibles, y dos uniones universales cuando se instale la válvula en caja o nicho.
- Todo el recorrido de agua caliente se encontrará protegido con material aislante térmico en base de lana de vidrio y/o asbesto en polvo.
- Las redes de agua fría y caliente serán probadas con bombas de mano a 100 lb/pulg² durante 15 minutos, sin que presenten fugas o pérdidas de presión.

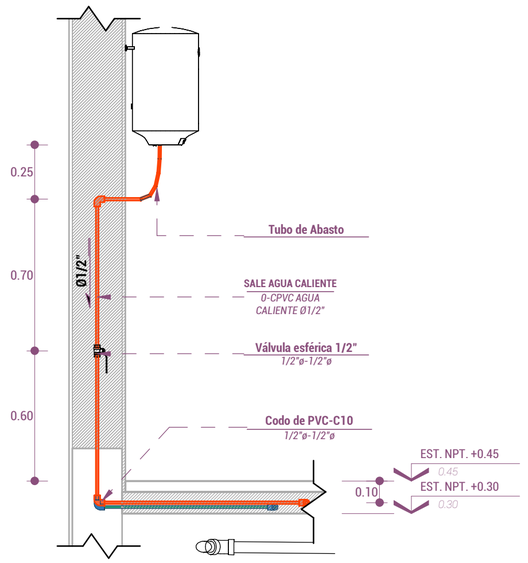


6 DETALLE DE IS CT. SERV.

1 : 20

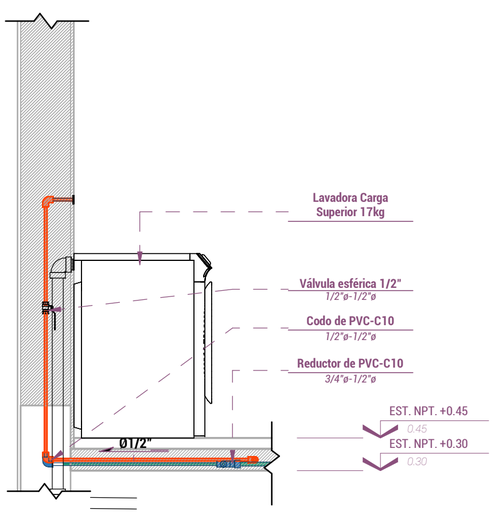


7 DETALLE DE IS LAVADORA

1 : 20

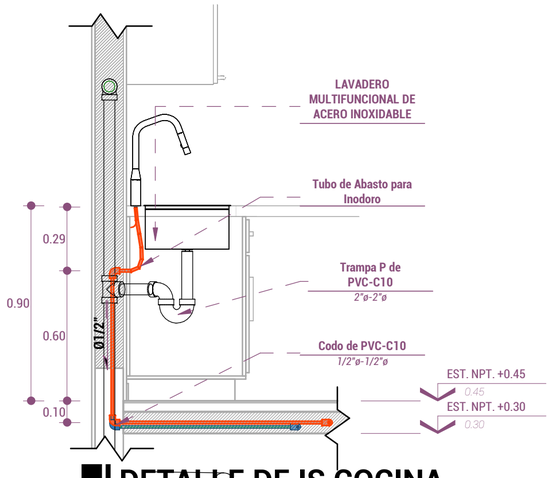


5 DETALLE DE IS COCINA

1 : 20

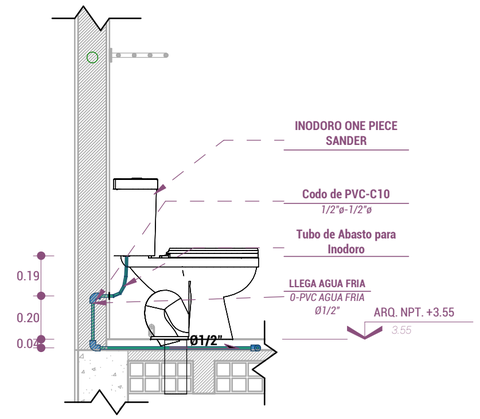

4 DETALLE DE IS SS.HH.

1 : 20

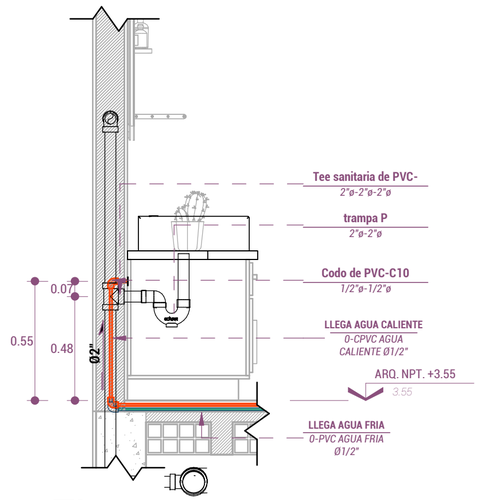

3 DETALLE DE IS LAVATORIOS

1 : 20

0 1 2 3 4 5 10 m

ANKA STUDIO

Proyecto:

VIVIENDA UNIFAMILIAR

Número de Proyecto: 0001

Estado del Proyecto:

Ubicación del Proyecto:

Puno - Perú

Nombre de Plano:

PLANIMETRIA AF/AC 3ER NIVEL

Cliente:	**ANKA Studio**
Dibujado por:	**ARQ. Yhovel Alex Merma Ari**
Revisado por:	**ING. Angel Yana**
Fecha:	**12/01/2025 8:22:38**
Escala:	**Como se indica**

Lámina No.

IS103