
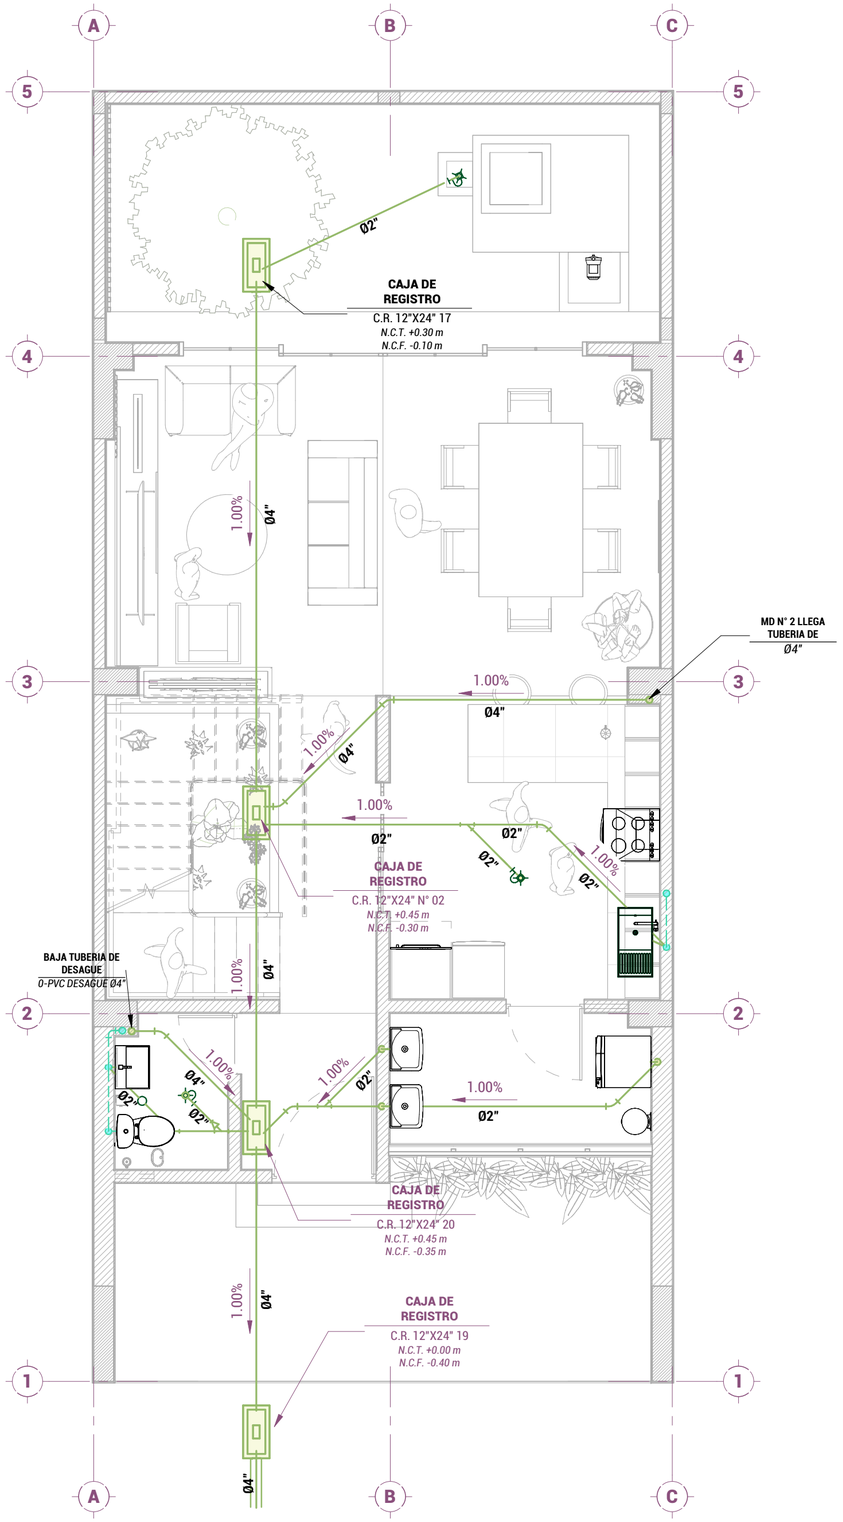


1 Planta general DESAGUE-1ER NIVEL


1 : 50

LEYENDA

DESAGÜE	
SÍMBOLO	**DESCRIPCIÓN**
	Caja de registro
	Tubería para desagüe – Conexión dom.
	Tubería de desagüe
	Tubería de ventilación
	Codo de 45° PVC
	Codo de 90° PVC
	Yee simple
	Yee doble
	Registro roscado en piso
	Trampa "P"
	Pendiente mínima de desagüe (S = 1.0%)
S =1.0%	Electrobomba

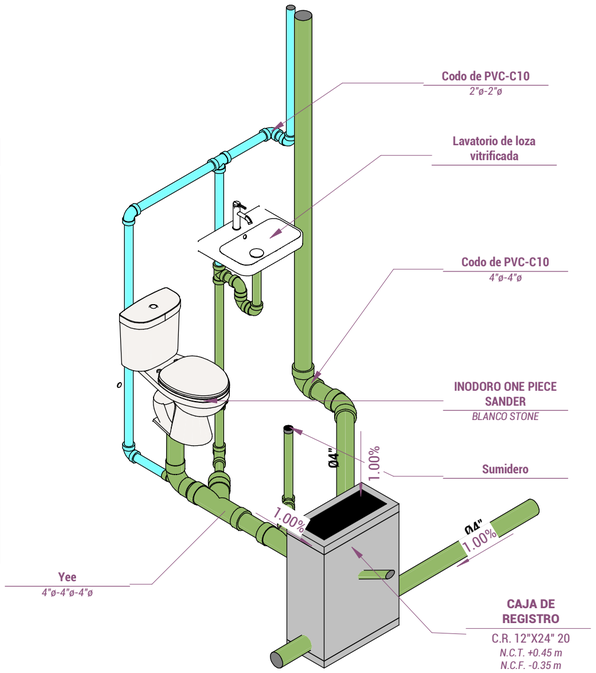

3 DETALLE DESAGÜE

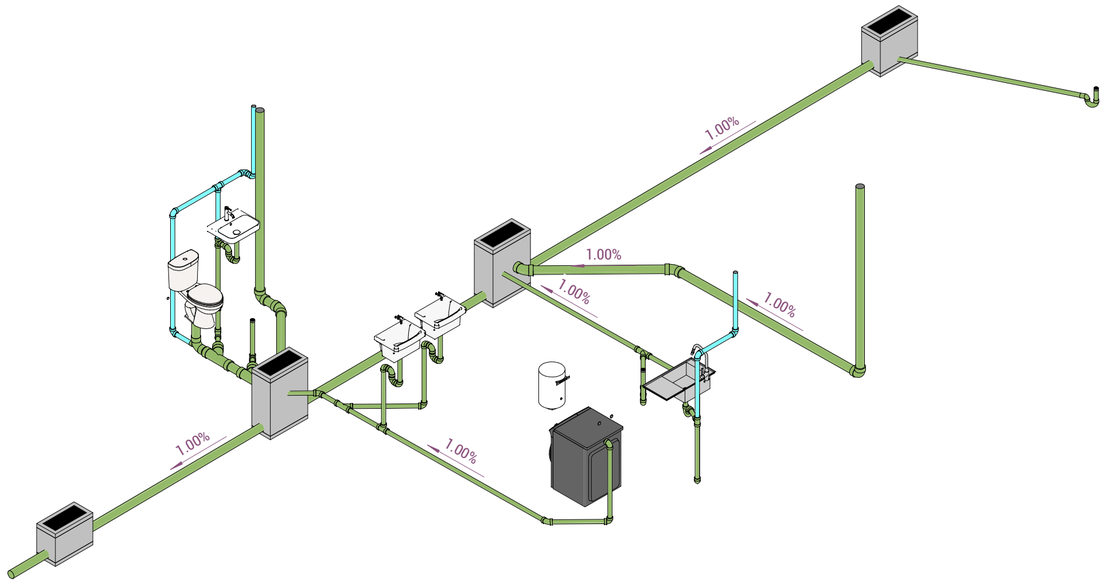

2 3D GENERAL DESAGUE 1ER NIVEL

0 1 2 3 4 5 10 m

ANKA STUDIO

Proyecto: **VIVIENDA UNIFAMILIAR**

Número de Proyecto: 0001

Estado del Proyecto:

Ubicación del Proyecto:

Puno - Perú

Nombre de Plano: **PLANIMETRIA DESAGUE 1ER NIVEL**

Cliente:	**ANKA Studio**
Dibujado por:	**ARQ. Yhovel Alex Merma Ari**
Revisado por:	**ING. Angel Yana**
Fecha:	**12/01/2025 8:22:55**
Escala:	**1 : 50**

Lámina No. **IS105**