
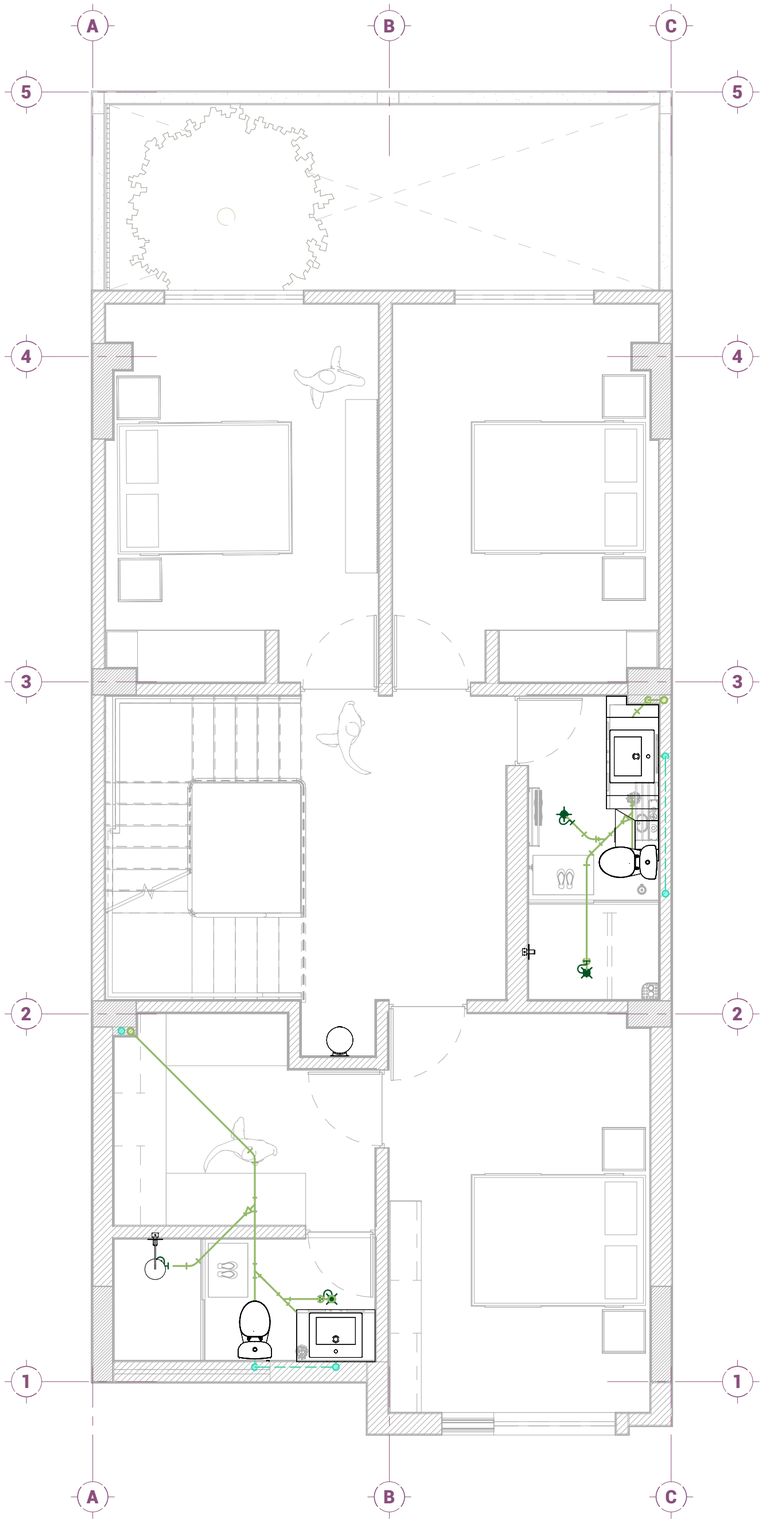



1 Planta general DESAGUE-2DO NIVEL

1 : 50

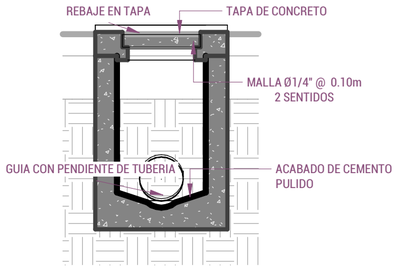


2 DETALLE DE CAJA DE REGISTRO

1 : 10

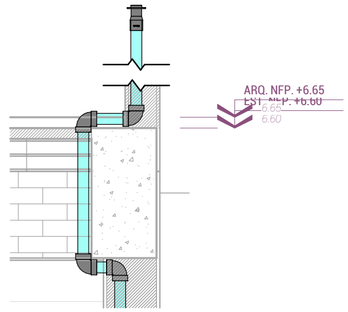

3 DETALLE TUBERIA VENTILACION

1 : 20

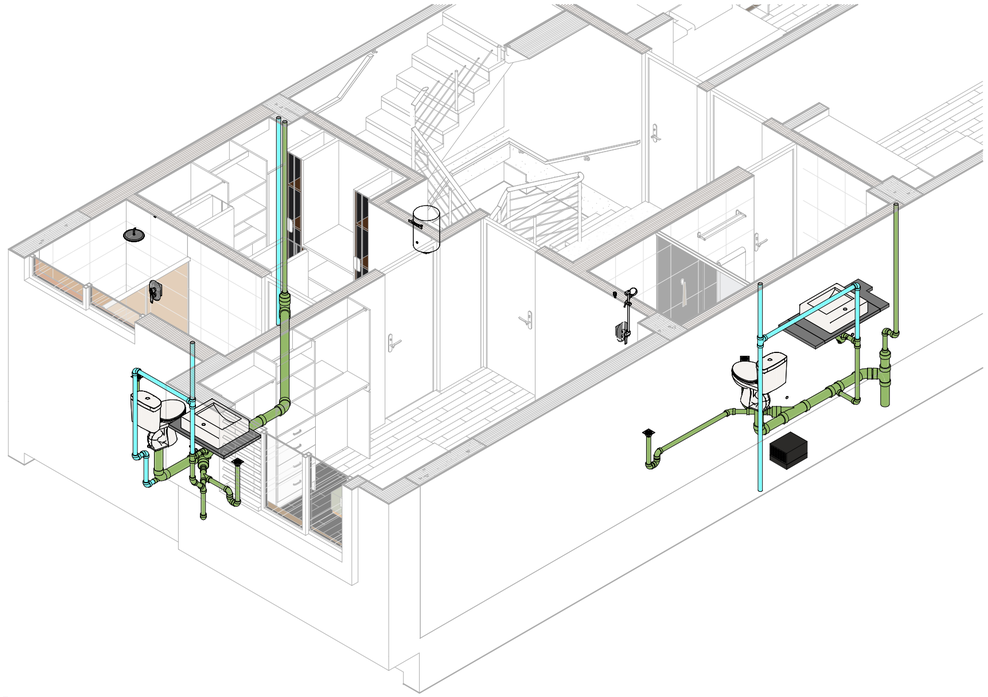

4 3D GENERAL DESAGUE 2DO NIVEL

0 1 2 3 4 5 10 m

ANKA STUDIO

Proyecto:
VIVIENDA UNIFAMILIAR

Número de Proyecto: 0001

Estado del Proyecto:

Ubicación del Proyecto:

Puno - Perú

Nombre de Plano:
PLANIMETRIA DESAGUE 2DO NIVEL

Cliente:	**ANKA Studio**
Dibujado por:	**ARQ. Yhovel Alex Merma Ari**
Revisado por:	**ING. Angel Yana**
Fecha:	**11/01/2025 18:52:50**
Escala:	**Como se indica**

Lámina No.
IS106